
# The whole farm · site baseline v2 (03 Oct 2026) with the old buildings · Taif / Palm House · STUDY

Design frame: origin M1 (the gate's east post), y along the M line southwards, x east. The deed (licence 798, 15/11/1440 H) gives the 20 corners; the field check of 03 Oct 2026 (44 tapes, rms 0.27 m) the gate, the M line, D, R, S, the palms, the lane wall; the v3 survey the well, the sheep barn, the shade house (measured), the workers' house and the service gate (estimated); the scanned deed sketch the old house and its annex (digitised, ± 1–3 m). Dotted boxes: no data, to be measured. Scale 1:450 on A3.

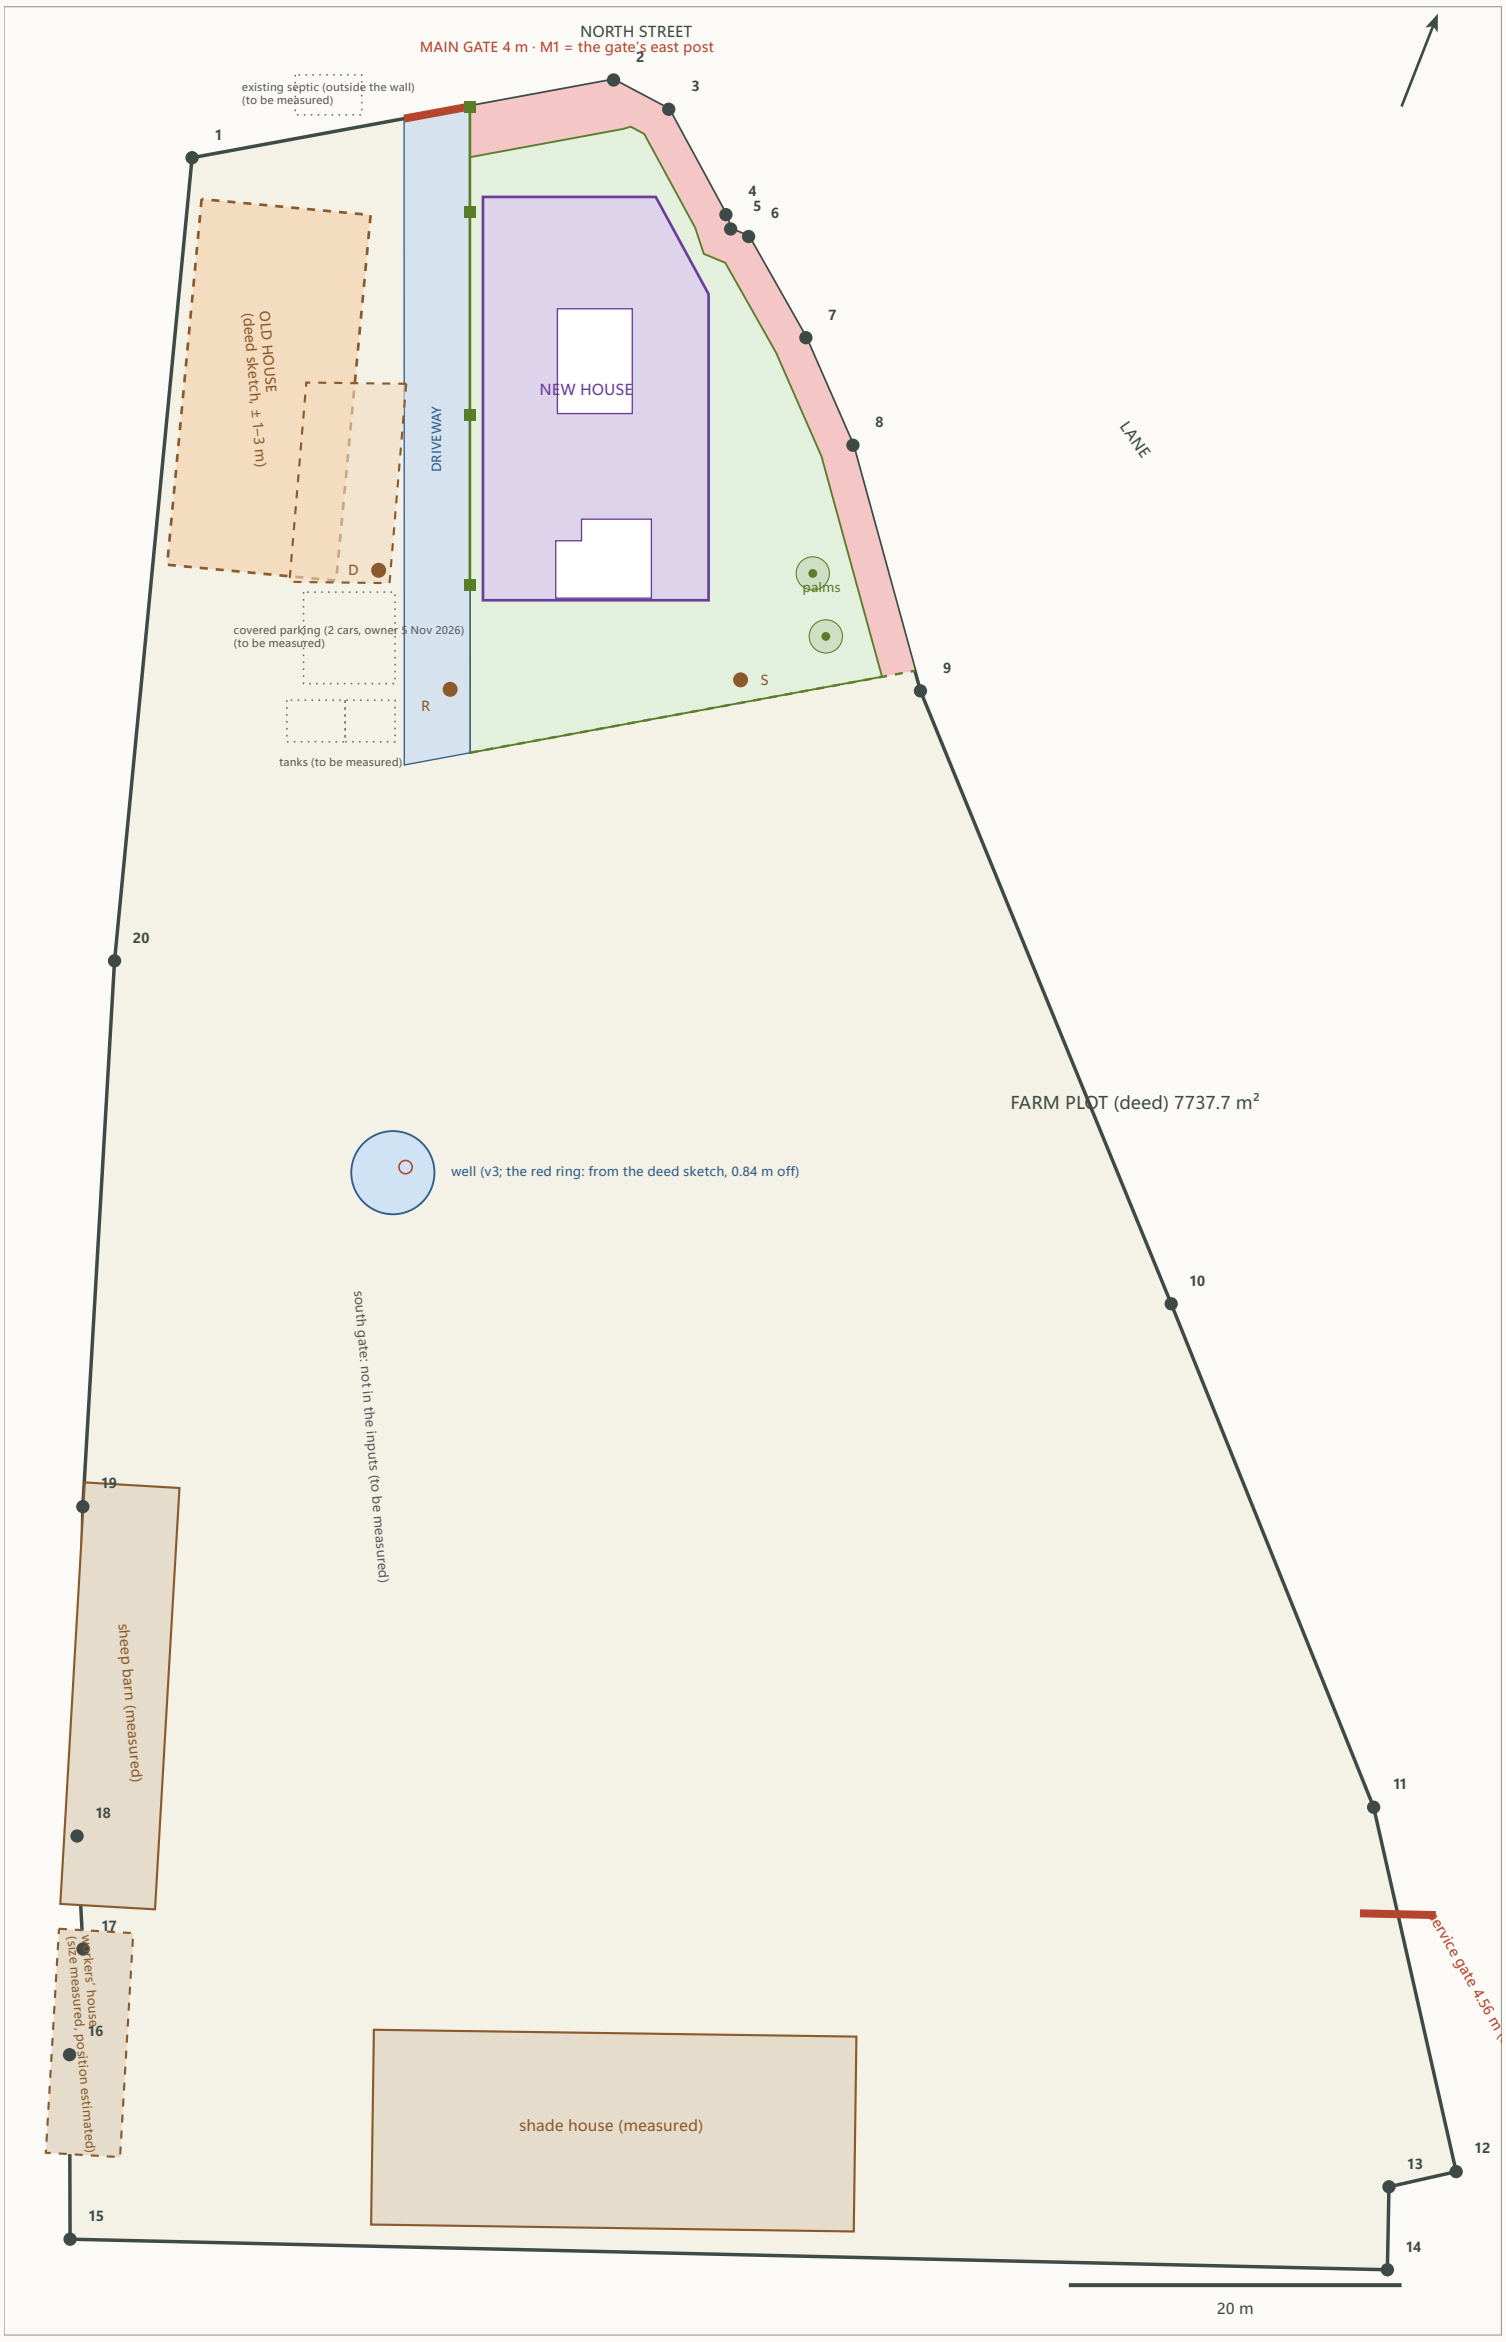


## Legend

- the farm plot (deed, 20 corners)
- the setbacks (3 m north street, 2 m lane) inside the build land
- the buildable envelope (to the illustrative south line)
- the driveway 4.00 m on the M line (decided)
- the new house (V8.3, shift 0.91 / 5.56)
- old buildings measured (v3)
- the old house and its annex from the deed sketch (± 1–3 m)
- no data: to be measured
- gates (the north 4 m main gate; the east service gate 4.56 m)

## Numbers

- Plot: 7737.7 m² from the 20 corners (deed 7 737.85). Build land to the illustrative south line 774.1 m²; envelope 667.8 m².
- The old house (deed sketch): a one-storey reinforced-concrete building ≈ 22.1 × 10.2 m (its envelope; the sketch shows an L) along the west boundary, 4.6 m from the new house's west wall, 3.8 m from the M line, 6.8 m from the nearest wall of the new house. Its annex ≈ 12 × 6 m touches the driveway's west edge (0 m; the field check puts the dakka 1.5 m clear: the sketch is ± 1–3 m); its south corner 1.01 m from D.
- The old majlis is PART OF the old house (owner, 5 Nov 2026): the guests' route to it is the driveway from the gate to the old house, 3.95 m wide, 4.6 m from the annex to the new house's west wall; the new house's paths are not touched.
- The covered parking (2 cars) and the existing ground tank are SOUTH of the old house, west of the driveway, near peg R (owner, 5 Nov 2026; the tank 3.4 m from R, the reserved tank west of it, 1 m between the parking and the tanks, the tanks 8 m from the new house); the septic outside the north wall near C1 serves the old house. Nothing of the farm lies south of the build land: the brief's south boxes are withdrawn.
- The palms 6 / 7.1 m from the new house; the well 32.3 m (ring edge); the service gate 89.2 m.

## To be measured on site

the old house's and the annex's corners (W1–W4, A1–A4), the covered parking's corners (P1–P4) and the tank's lid / fill point (K0, K1): the field sheet in `docs/SITE_SETOUT.md` § 8; the reserved tank's place; the septic (position, lids, inlet level, capacity for both houses, the old house's connection); where guests park; the south gate; the workers' house position; the service gate position. Peg S lies 5.5 m from palm 2's trunk: check it on site.

# The north zone enlarged · the new house at the current position (shift 0.91, 5.56) and the old house

1:220 on A3 · y −6 … 52 m




## What the sketch says

The scanned deed carries a plan sketch of the plot with two hatched buildings near corner 1 on the west boundary: the larger one labelled بناء دور مسلح (a one-storey reinforced-concrete building: the old house) and a thin-line ملحق (annex) on its north-east side towards the driveway, plus the stores (مستودعات: the shade house, measured in v3) in the south. The sketch was georeferenced on seven deed corners (1, 2, 3, 12, 13, 14, 15; rms 1.36 m) and checked on the well (0.84 m from the v3 well) and on the dakka corner D (the annex's south corner 1.01 m from it): the sketch sits within about 1 m of the field. The buildings' corners are read from a 300 dpi scan at ≈ 7.3 px per metre: ± 1–3 m.

## Position of the old house in the design frame

| Corner | x east | y along M |
|---|---|---|
| W1 | −16.13 | 5.57 |
| W2 | −18.2 | 27.56 |
| W3 | −8.04 | 28.51 |
| W4 | −5.97 | 6.53 |
| A1 | −3.83 | 16.67 |
| A2 | −4.83 | 28.66 |
| A3 | −10.85 | 28.58 |
| A4 | −9.83 | 16.6 |

## Does anything conflict?

- **The new house, the driveway and the paths:** no. The old house is 4.6 m west of the new house's west wall and 3.8 m west of the M line; the driveway (x −3.95 … 0) runs between them and keeps its 3.95 m; the guest path on the driveway's east edge and the fire vehicle's stand are unaffected. The annex's east edge sits on the driveway's west edge (0 m): within the sketch's tolerance; the field check gives the dakka 1.5 m clear.
- **The service yard, the garden, the outdoor kitchen:** all on the east and south; nothing of the old house reaches them.
- **The owner's answers (5 Nov 2026):** the old house is WEST of the driveway as on the deed sketch (confirmed; its corners still to be measured); the old majlis is PART OF it (no separate building); the covered parking for two cars and the existing ground tank are SOUTH of the old house, west of the driveway near peg R (the tank is NOT in the new house's garden; the reserved tank goes next to it, west); the septic outside the north wall near C1 serves the old house and takes the new house's drains (site plan page 4: the route, 37.9 m from the yard's chamber, the falls, a chamber at every bend, the driveway crossed once; its capacity for both houses, its inlet level and a pump are flagged for the engineer and the survey). Nothing of the farm lies south of the build land: the brief's south boxes (old house, parking, tank, farm parking) are withdrawn. **Where guests park is to be asked.**
- **The carport and the tanks against each other and the new house:** 1 m between the carport and the tanks (no clash); the car route gate → driveway → a right turn into the carport (open to the east) is the owner's existing one; the water truck stands on the driveway beside the tanks; the tanks 8 m from the new house; the supply pipe crosses the driveway once (y 36.5) to the guest path band and the utility room.
- **Corner C1:** the deed puts the plot's north-west corner at x −16.7, 10 m further west than the site plan's old C1 (−6.5); the septic "near C1" stays approximate: to be measured (its lids, its inlet level).

Whole-farm study checks passed (7): the 20 deed corners close to the deed area 7 737.85 m² (7737.7 m², rigid transform from UTM) · M1 is the origin and M4 lies on the M line 28.80 m south (28.8) · the well digitised from the deed sketch lies within 2 m of the v2 well (0.84 m): the georeferencing check · the annex's south corner lies within 2 m of the fitted dakka corner D (1.01 m): the sketch and the field agree · the new house's walls lie inside the buildable envelope · the old house (deed sketch) is clear of the new house (6.8 m), the M line (3.8 m) and the driveway's east edge; its annex touches the driveway's west edge (0 m) · the covered parking and the tanks (owner, 5 Nov 2026) lie west of the driveway and south of the old house (y ≥ 28.7), 1 m apart, the existing tank 3.4 m from peg R and the tanks 8 m from the new house (≥ 5).