
West wash block · family + guest · layout study

Taif / Palm House · Ground floor V10.0 (the owner's review, 10 Nov 2026) · block 2.75 × 13.6 m = 37.4 m² · scale 1 m = 1.35 cm · north up

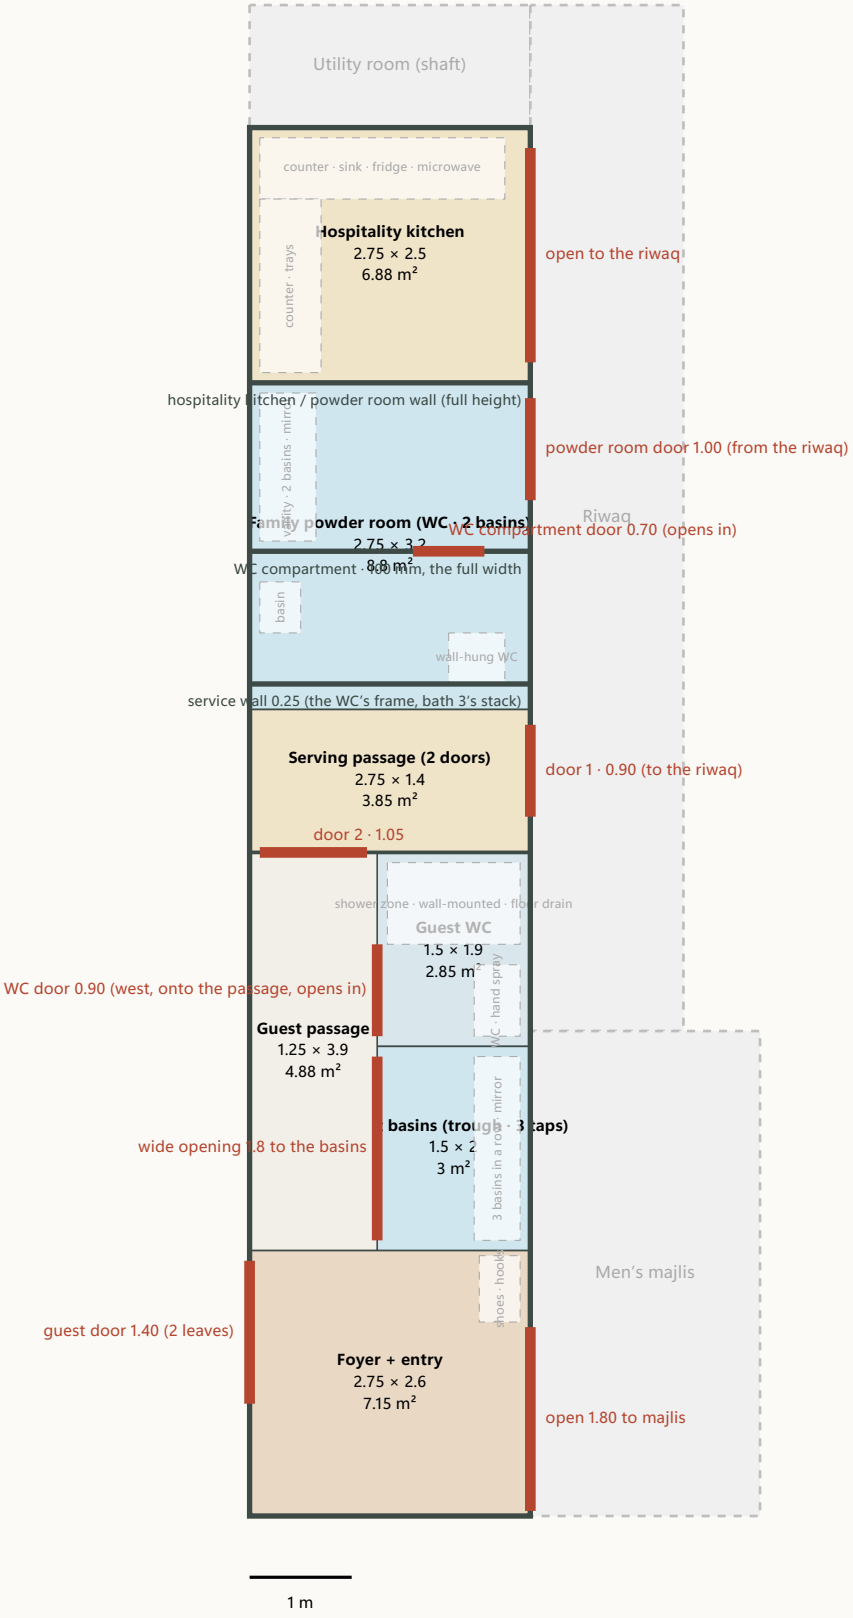

Rooms

Room	w × d (m)	m²
Hospitality kitchen	2.75 × 2.5	6.88
Family powder room (WC · 2 basins)	2.75 × 3.2	8.8
Serving passage (2 doors)	2.75 × 1.4	3.85
Guest WC	1.5 × 1.9	2.85
Guest basins (trough · 3 taps)	1.5 × 2	3
Guest passage	1.25 × 3.9	4.88
Foyer + entry	2.75 × 2.6	7.15
Block	2.75 × 13.6	**37.4**

✓ **All rooms inside the block, no overlaps, no gaps**

Route

Guests: double door (north end of the foyer's west wall) → foyer: shoes and bisht on the wall opposite → turn south → 1.80 m opening into the men's majlis (south end of the east wall). For washing: foyer → guest passage → the three basins (a wide opening) and the WC (its own door, next to them).
Family: riwaq → hospitality kitchen (open, no door) · the family **powder room** (one door from the riwaq; the two basins under the mirror in the open zone facing the door, the WC compartment across the far end with its own door, a WC and one basin).
Serving: hospitality kitchen or main kitchen → riwaq → door 1 → **serving passage** → door 2 → guest passage → foyer → majlis. The two doors are never open together: the family leaves the tray, closes door 1 and calls the host; the host opens door 2 and collects. Door 1 locks from the riwaq side, door 2 from inside the passage, so the family controls both. The guest side has no door onto the riwaq.

Rules

- Hospitality kitchen 2.75 × 2.5 (≈ 5.8 m² clear): light (clean) kitchen for coffee, tea, dates, desserts and reheating; the serving base for the men's majlis. Open to the riwaq, no door, no hob. L-counter on the north and west walls with a small sink, under-counter fridge, microwave, kettle and coffee things; cups and trays stored there; small extract fan. The main east kitchen is the heavy (dirty) kitchen.
- A full-height wall separates the hospitality kitchen from the powder room; the kitchen opens only to the riwaq, the powder room has its own door.
- **Family powder room 2.75 × 3.2 (≈ 7.6 m² clear; 10 Nov 2026, owner: redrawn simple and rectangular):** the **WC compartment across the full width** at the south end (y 14.55–16.1 CSV, 2.75 × 1.55 on axes, ≈ 2.55 × 1.38 clear; a 100 mm partition; its own 0.70 door at x 1.6–2.3, opening in) with **only the WC** (wall-hung, on the south 0.25 service wall at the east end: its frame and bedroom 3's stack inside the wall, an access panel from the serving passage) **and one basin** on the west wall; **outside, the open zone in front of the entrance** (y 12.9–14.55, 2.75 × 1.65, ≈ 2.55 × 1.5 clear; the door 1.00 from the riwaq, x 2.75, y 13.05–14.05) with **exactly two basins under a large mirror** on the west wall (a 1.45 m vanity), cove lighting; **no shower**. Swings: the entrance door sweeps x 1.75–2.75, the compartment door x 1.6–2.3 inside the compartment: both clear of the basins and the WC; a person at the two basins (x 0.65–1.2) does not stand in front of the compartment door. The drains 0.5 m into the west buried run; the hidden beam B14 (y 14.4) becomes a drop beam or the slab spans 3.2 m (the engineer).
- Serving passage 2.75 × 1.4 on axes, 1.20 m clear, no shelf and no fixed equipment; door 1 0.90 m to the riwaq, door 2 1.05 m to the guest passage. Opposite door 1 the living's west wall is solid and full height (the TV wall, V6.3); privacy rests on the two doors.20 m low partition, so privacy rests on the two doors.
- **Guest WC 1.5 × 1.9 (≈ 1.3 × 1.7 clear; 10 Nov 2026, owner: redrawn):** a clean rectangle east of the guest passage (x 1.25–2.75, y 17.5–19.4 CSV) with **its own 0.90 door on the passage** (the west wall, y 18.4–19.3, opening in); inside **only the WC** (with its hand spray, in the south-east corner, facing west) **and a wall-mounted shower with mixer** on the north wall over a floor drain with falls (the wet zone 1.3 × 0.8 at the north end), the whole room tanked and tiled;

no basin, no cubicle wall, no tray, nothing diagonal. The door's swing (x 1.25–2.15, y 18.4–19.3) clears the WC (x 2.2–2.65).

- **Guest basins 1.5 × 2.0 (≈ 1.3 × 1.8 clear; 10 Nov 2026, redrawn):** the rectangle right next to the WC (x 1.25–2.75, y 19.4–21.4 CSV), open to the guest passage through a **1.8 m wide opening** (y 19.5–21.3); **three basins in one straight row** on the east wall (1.8 m: three bowls at 0.6 m) under a mirror. A guest at the basins stands inside this room (x 1.6–2.2), not in the passage and not in front of the WC's door, which is 0.1 m north of the opening.
- Foyer 2.75 × 2.6: double door 1.40 m (two leaves, opening in) at the north end of the west wall; 1.80 m opening, no door, at the south end of the east wall (≈ 0.65 m of wall left at its north end for the shoe cabinet and hooks). The two openings overlap by ≈ 0.75 m along the foyer, so the bent entry is only partial: from the door a guest sees a strip of the majlis; a curtain or a short screen in front of the opening would close it.
- One strip of wet rooms on one drain run, the west buried run (hospitality kitchen sink, the powder room's three basins and WC, the guest WC's floor drain and WC, the three guest basins), cleanout under the serving passage. First-floor bathrooms stack over the north part of the block, near the shaft.