
# West wash block · family + guest · layout study

Taif / Palm House · Ground floor V4.0 · block 2.75 × 13.6 m = 37.4 m² · scale 1 m = 1.35 cm · north up

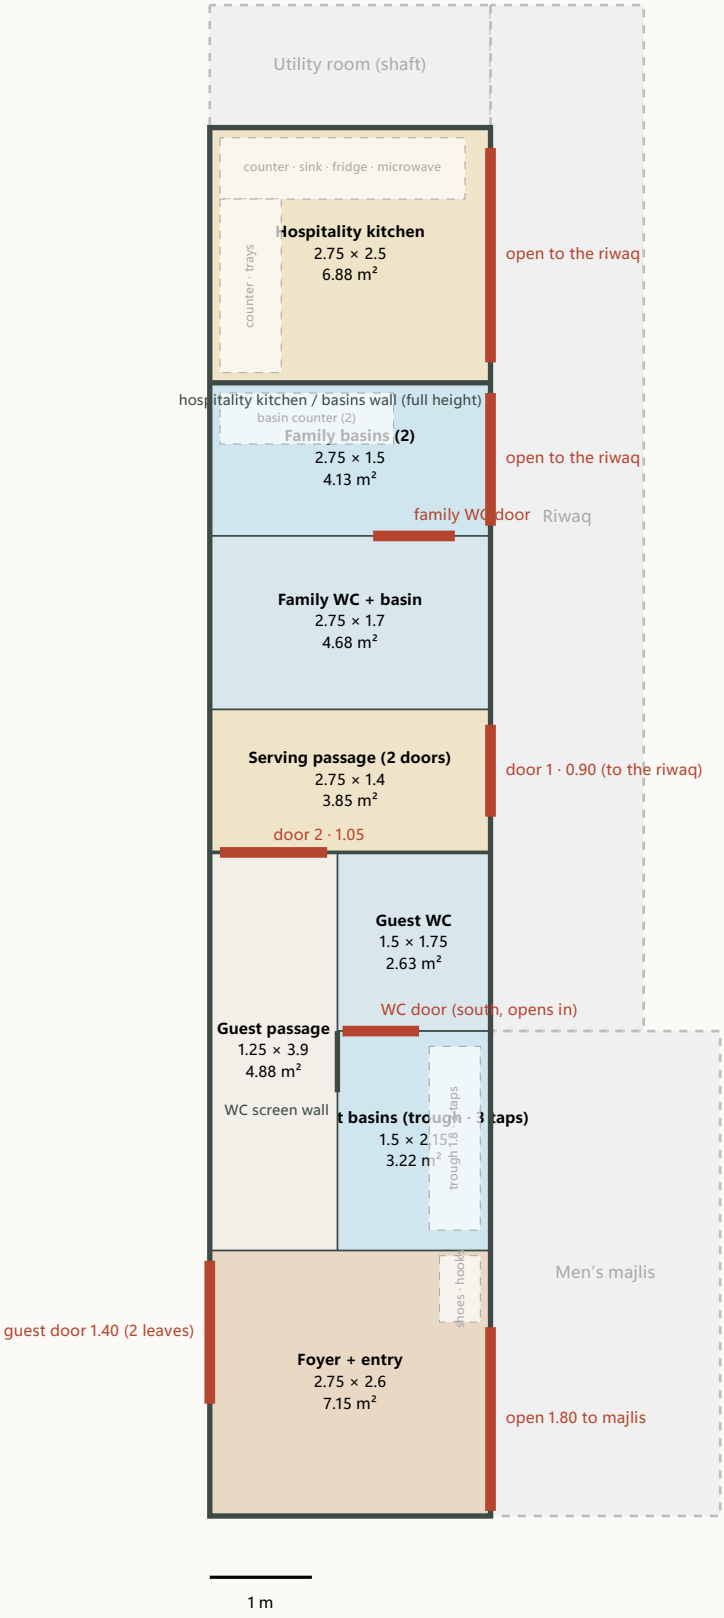


## Rooms

| Room | w × d (m) | m² |
|---|---|---|
| Hospitality kitchen | 2.75 × 2.5 | 6.88 |
| Family basins (2) | 2.75 × 1.5 | 4.13 |
| Family WC + basin | 2.75 × 1.7 | 4.68 |
| Serving passage (2 doors) | 2.75 × 1.4 | 3.85 |
| Guest WC | 1.5 × 1.75 | 2.63 |
| Guest basins (trough · 3 taps) | 1.5 × 2.15 | 3.22 |
| Guest passage | 1.25 × 3.9 | 4.88 |
| Foyer + entry | 2.75 × 2.6 | 7.15 |
| **Block** | 2.75 × 13.6 | **37.4** |

✓ **All rooms inside the block, no overlaps, no gaps**

## Route

**Guests:** double door (north end of the foyer's west wall) → foyer: shoes and bisht on the wall opposite → turn south → 1.80 m opening into the men's majlis (south end of the east wall). For washing: foyer → guest passage → trough basin and WC.

**Family:** riwaq → hospitality kitchen (open, no door) · family basins (open, no door) → family WC (door off the basins).

**Serving:** hospitality kitchen or main kitchen → riwaq → door 1 → **serving passage** → door 2 → guest passage → foyer → majlis. The two doors are never open together: the family leaves the tray, closes door 1 and calls the host; the host opens door 2 and collects. Door 1 locks from the riwaq side, door 2 from inside the passage, so the family controls both. The guest side has no door onto the riwaq.

## Rules

- Hospitality kitchen 2.75 × 2.5 (≈ 5.8 m² clear): light (clean) kitchen for coffee, tea, dates, desserts and reheating; the serving base for the men's majlis. Open to the riwaq, no door, no hob. L-counter on the north and west walls with a small sink, under-counter fridge, microwave, kettle and coffee things; cups and trays stored there; small extract fan. The main east kitchen is the heavy (dirty) kitchen.
- A full-height wall separates the hospitality kitchen from the family basins; each opens only to the riwaq.
- Family basins (2): a straight counter, no cupboards opposite (≈ 0.75–0.8 m in front, plus the open riwaq).
- Family WC 2.75 × 1.7: WC and basin, no shower (showers are on the first floor). Door off the basin niche.
- Serving passage 2.75 × 1.4 on axes, 1.20 m clear, no shelf and no fixed equipment; door 1 0.90 m to the riwaq, door 2 1.05 m to the guest passage. Opposite door 1 the living room has only a 1.20 m low partition, so privacy rests on the two doors.
- Guest WC 1.5 × 1.75 (≈ 1.3 × 1.55 clear), its south wall on the same line as the men's majlis north wall. WC and hand spray only; door in the south wall, opening in, hidden from the passage by a 0.6 m screen wall.
- Guest basins: one trough ≈ 1.8 m with three taps on the east wall, open to the guest passage (≈ 1.025 m clear).
- Foyer 2.75 × 2.6: double door 1.40 m (two leaves, opening in) at the north end of the west wall; 1.80 m opening, no door, at the south end of the east wall (≈ 0.65 m of wall left at its north end for the shoe cabinet and hooks). The two openings overlap by ≈ 0.75 m along the foyer, so the bent entry is only partial: from the door a guest sees a strip of the majlis; a curtain or a short screen in front of the opening would close it.
- One strip of wet rooms on one drain run (hospitality kitchen sink, family basins, family WC, guest WC, trough), cleanout under the serving passage. First-floor bathrooms stack over the north part of the block, near the shaft.