
# East service block · kitchen, laundry, maid wing, air tower · layout study

Taif / Palm House · Design V3 (Z4) · block = CSV x 9–13, y 0–12.5 (NE corner cut) · 42 m² · scale 1 m = 1.3 cm · north up

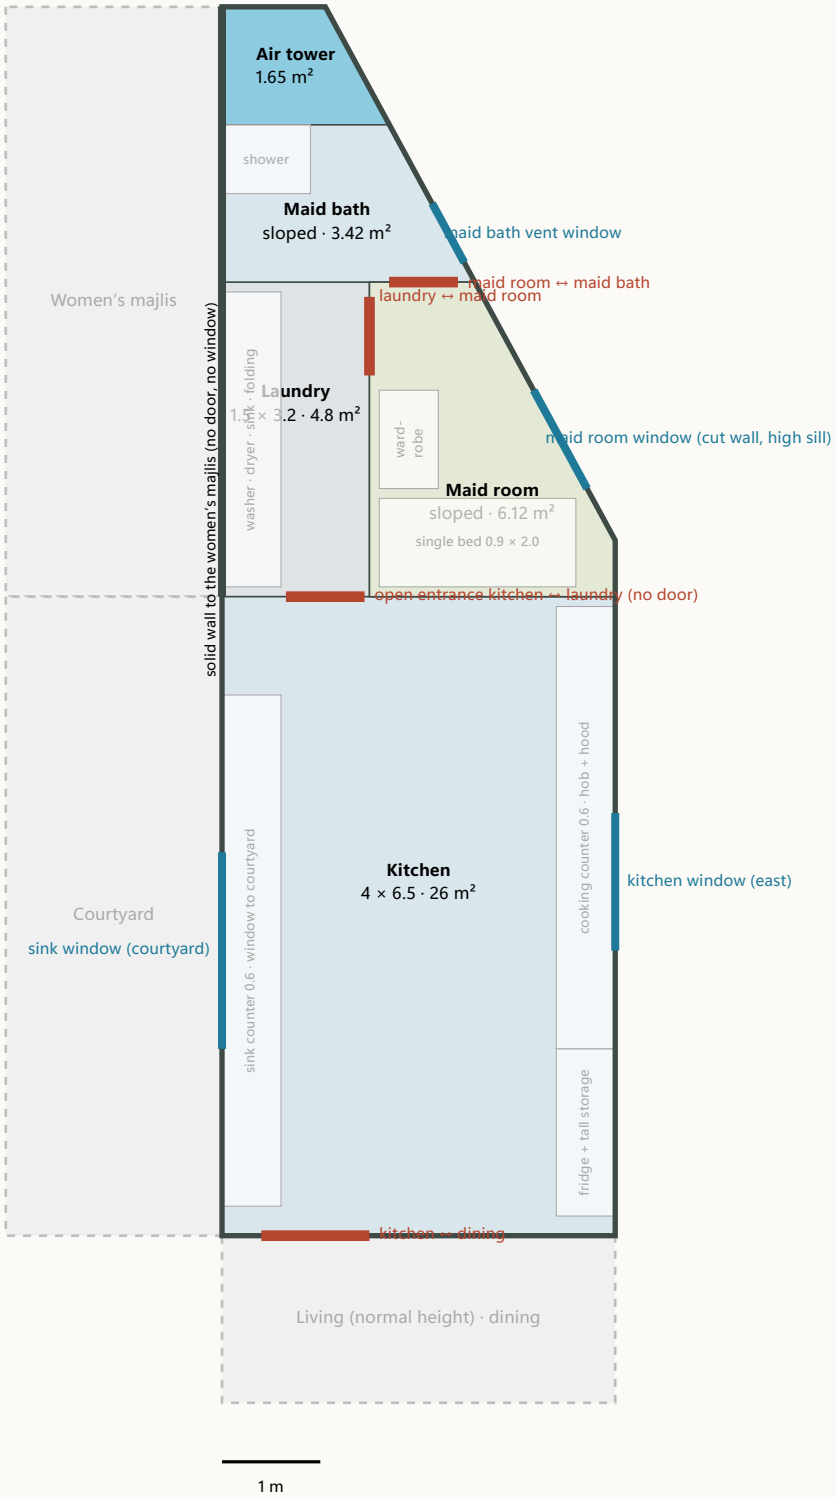


## Rooms

| Room | w × d (m) | m² |
|---|---|---|
| Maid bath | sloped (to the cut wall) | 3.42 |
| Maid room | sloped (to the cut wall) | 6.12 |
| Laundry | 1.5 × 3.2 | 4.8 |
| Kitchen | 4 × 6.5 | 26 |
| Air tower (polygon) | 4 corners | 1.65 |
| Leftover slivers along the cut | | 0 |
| **Block** | | **42** |

✓ **All rooms inside the block, no overlaps**

## Route

**Family:** living (normal height) · dining → kitchen (south door).
**Maid:** kitchen → laundry → maid room → maid bath. No external door and no other door: all her movement passes through the kitchen.
**Cooking:** sink on the courtyard wall, hob and hood on the east (outside) wall, so heat and smoke leave the house; fridge and tall storage at the south-east, next to the dining door.

## Rules

- Kitchen isolated: doors only to the dining area (south) and the laundry (north). No door to the courtyard, riwaq or women's majlis.
- Kitchen 4 × 6.5 m (26 m²), y 6.0–12.5, exactly on the courtyard lines. Sink run on the courtyard wall, hob and hood on the east wall (4.5 m), fridge and tall storage at the south-east; aisle ≈ 2.6 m. No island (only 0.6 m deep would fit); room for a small breakfast table.
- Laundry vertical on the west wall (women's majlis side), 1.5 × 3.2 m (x 0–1.5, y 2.8–6.0), from the kitchen up to the maid bath: open entrance from the kitchen in its south wall (no door); washer, dryer, utility sink and folding counter in one line on the west wall (solid, no opening); 0.9 m walkway; maid room door at the north end of its east wall. The maid's only route. No outside wall: needs a mechanical extract fan to the roof.
- Maid room east of the laundry, from y 2.8 down to y 6.0 and up to the sloped cut wall (≈ 6.1 m² on centre lines, ≈ 5.3 m² clear, under the 6.5 m² target): door from the laundry at the north end of its west wall and door to the maid bath in its north wall, both in the narrow north part; single bed 0.9 × 2.0 along the south wall (the widest part, 2.5 m) and a wardrobe on the west wall; window in the cut wall with a high sill (lane side, privacy).
- Main cross walls on the house lines: y 6.0 (women's majlis / courtyard) and y 12.5 (dining).
- Maid bath 1.6 m deep, running up to the cut wall (≈ 3.42 m²): WC, basin, compact shower; vent window in the cut wall; door only from the maid room.
- Solid wall (no door, no window) between the maid wing and the women's majlis.
- Air tower in the tip of the cut corner, ≈ 1.1 m² clear, takes no room space; cleaning from a roof hatch.
- One east wet stack: maid bath, laundry sink and kitchen sink on one drain line down the block; cleanout access in the laundry.

Edit the lists at the top: rooms-data, fixtures, doors, windows, solid, neighbours. Main CSV = local + (9, 0).