
The whole farm · site baseline v2 (03 Oct 2026) with the old buildings · Taif / Palm House · STUDY

Design frame: origin M1 (the gate's east post), y along the M line southwards, x east. The deed (licence 798, 15/11/1440 H) gives the 20 corners; the field check of 03 Oct 2026 (44 tapes, rms 0.27 m) the gate, the M line, D, R, S, the palms, the lane wall; the v3 survey the well, the sheep barn, the shade house (measured), the workers' house and the service gate (estimated); the scanned deed sketch the old house and its annex (digitised, ± 1–3 m). Dotted boxes: no data, to be measured. Scale 1:450 on A3.

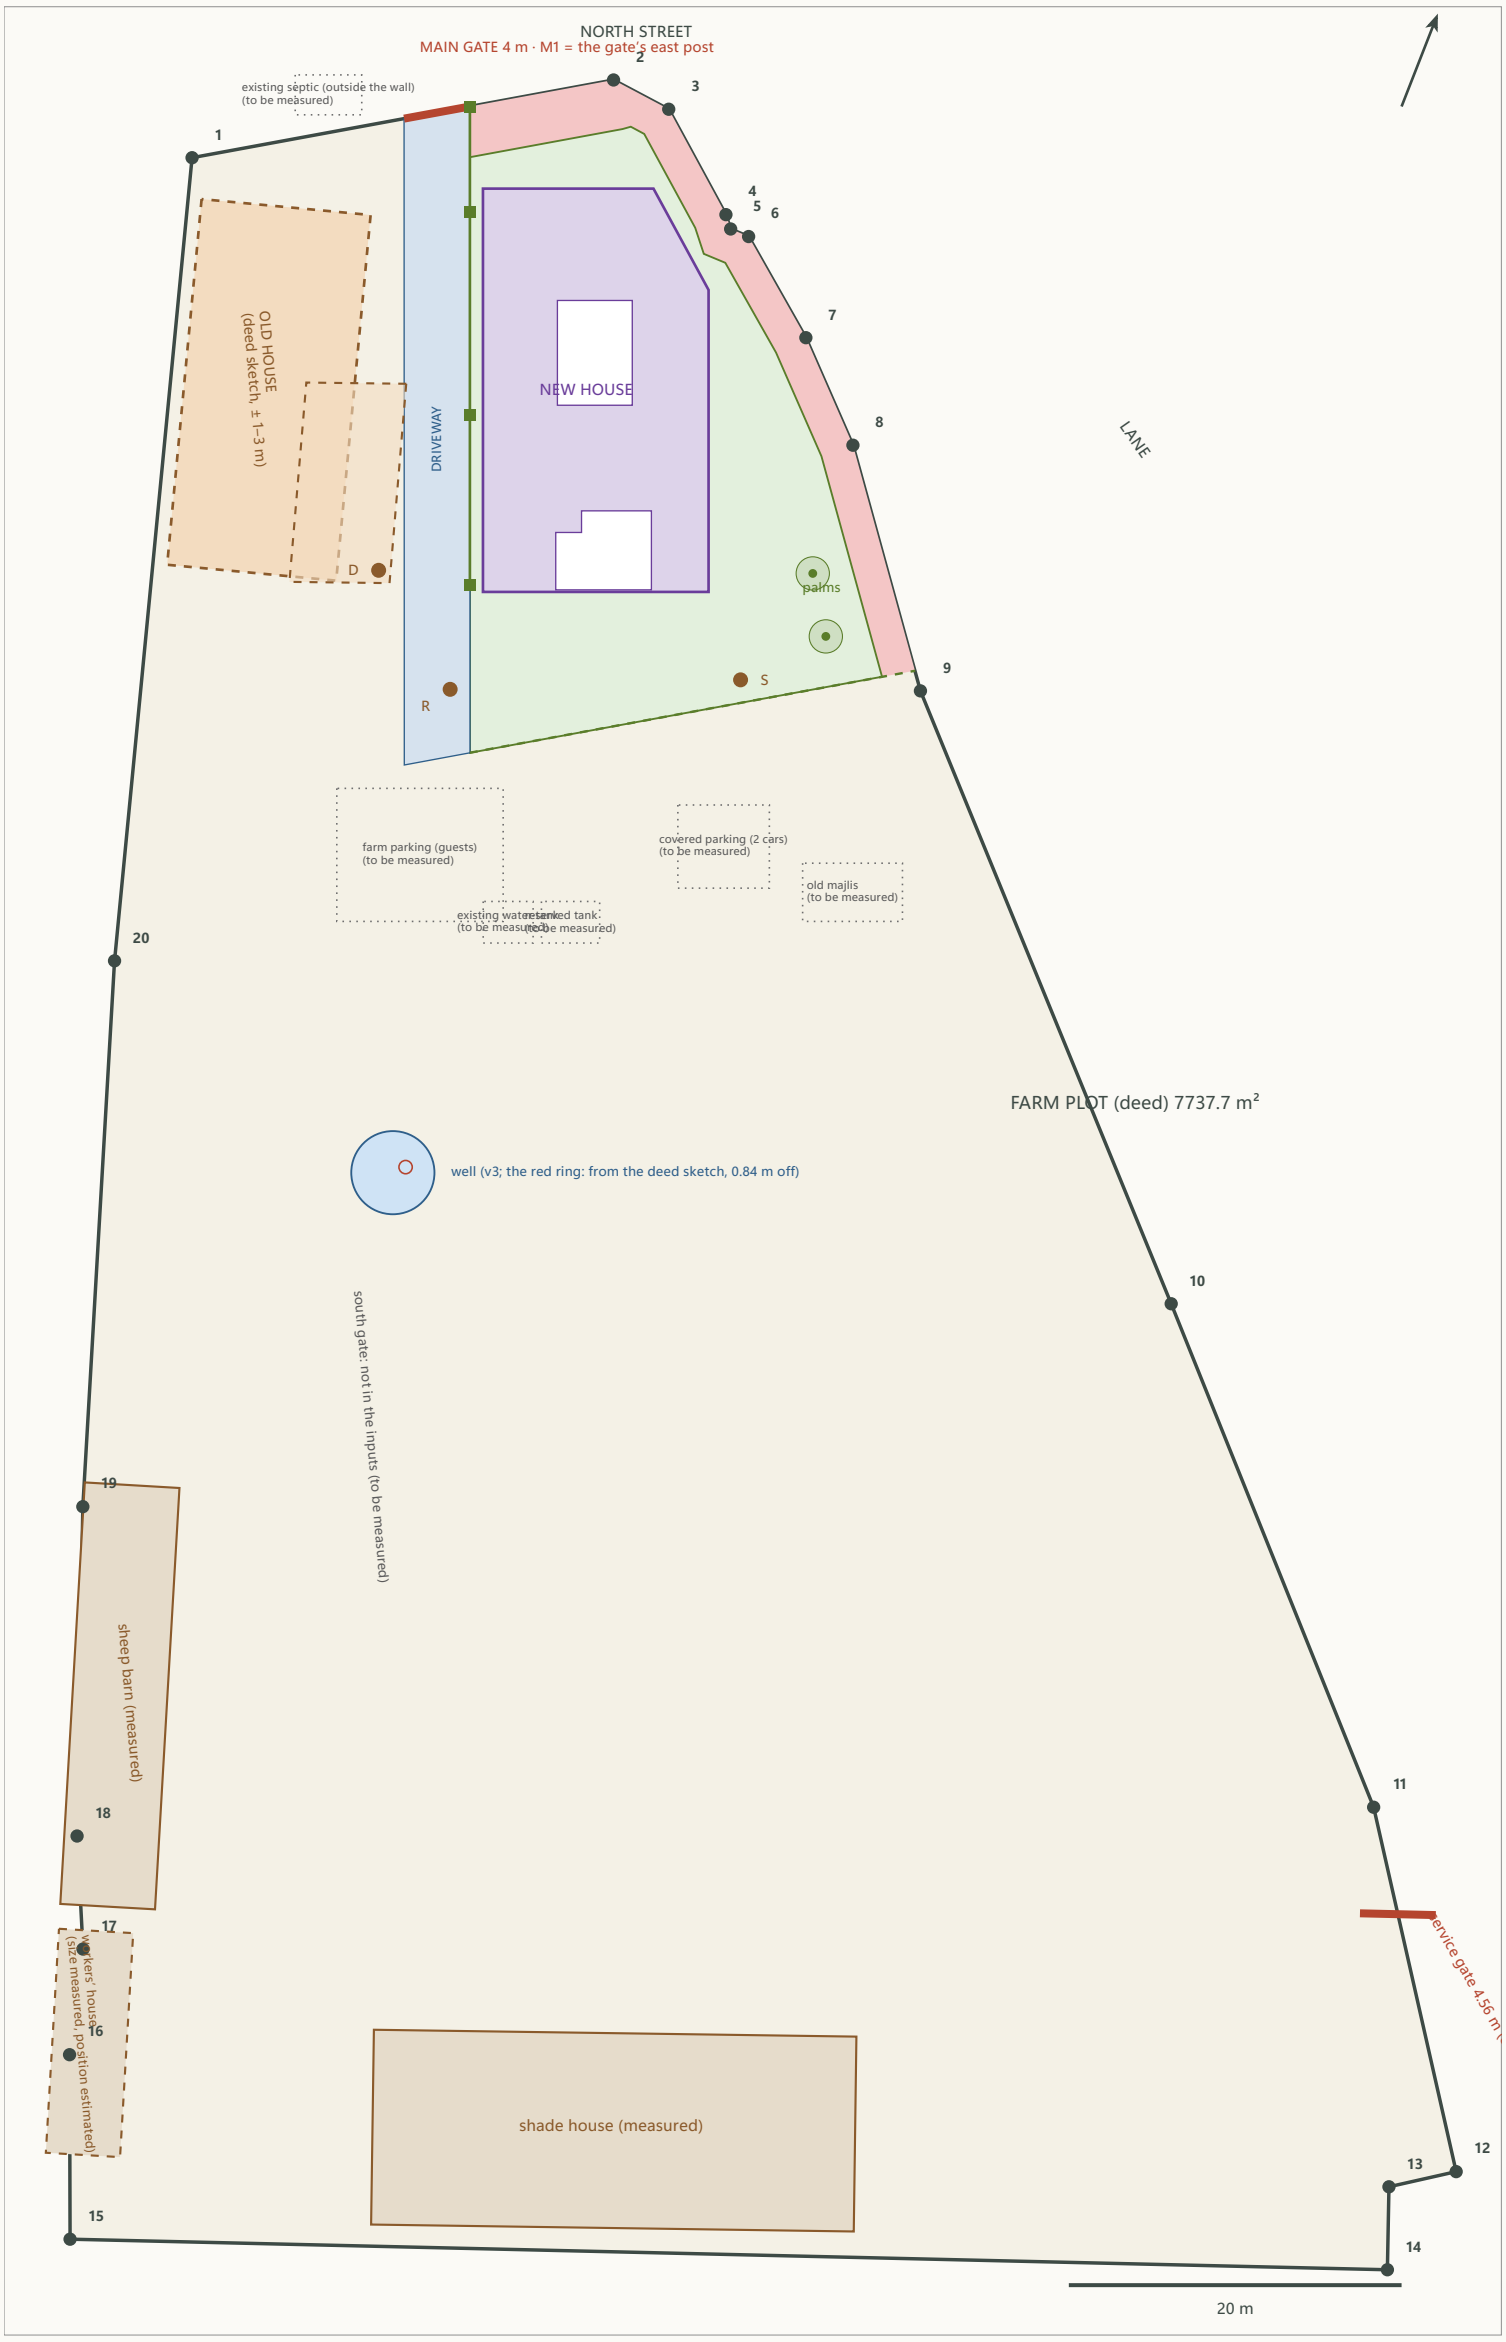

Legend

- the farm plot (deed, 20 corners)
- the setbacks (3 m north street, 2 m lane) inside the build land
- the buildable envelope (to the illustrative south line)
- the driveway 4.00 m on the M line (decided)
- the new house (V8.3, shift 0.91 / 5.06)
- old buildings measured (v3)
- the old house and its annex from the deed sketch (± 1–3 m)
- no data: to be measured
- gates (the north 4 m main gate; the east service gate 4.56 m)

Numbers

- Plot: 7737.7 m² from the 20 corners (deed 7 737.85). Build land to the illustrative south line 774.1 m²; envelope 667.8 m².
- The old house (deed sketch): a one-storey reinforced-concrete building ≈ 22.1 × 10.2 m (its envelope; the sketch shows an L) along the west boundary, 4.6 m from the new house's west wall, 3.8 m from the M line, 6.8 m from the nearest wall of the new house. Its annex ≈ 12 × 6 m touches the driveway's west edge (0 m; the field check puts the dakka 1.5 m clear: the sketch is ± 1–3 m); its south corner 1.01 m from D.
- The route to the old majlis (assumed position) passes between the old buildings and the new house: the narrowest clear width is the driveway's 3.95 m plus the west strip, 4.6 m from the annex to the new house's west wall.
- The palms 6 / 7.3 m from the new house; the well 32.8 m (ring edge); the service gate 89.7 m.

To be measured on site

the old house's and the annex's corners (W1–W4, A1–A4: the field sheet in `docs/SITE_SETOUT.md` § 8); the old majlis; the covered parking; the farm parking; the existing water tank and the reserved tank's place; the septic (position, inlet, capacity); the south gate; the workers' house position; the service gate position. Peg S lies 5.5 m from palm 2's trunk: check it on site.

The north zone enlarged · the new house at the current position (shift 0.91, 5.06) and the old house

1:220 on A3 · y −6 … 52 m



What the sketch says

The scanned deed carries a plan sketch of the plot with two hatched buildings near corner 1 on the west boundary: the larger one labelled بناء دور مسلح (a one-storey reinforced-concrete building: the old house) and a thin-line ملحق (annex) on its north-east side towards the driveway, plus the stores (مستودعات: the shade house, measured in v3) in the south. The sketch was georeferenced on seven deed corners (1, 2, 3, 12, 13, 14, 15; rms 1.36 m) and checked on the well (0.84 m from the v3 well) and on the dakka corner D (the annex's south corner 1.01 m from it): the sketch sits within about 1 m of the field. The buildings' corners are read from a 300 dpi scan at ≈ 7.3 px per metre: ± 1–3 m.

Position of the old house in the design frame

Corner	x east	y along M
W1	−16.13	5.57
W2	−18.2	27.56
W3	−8.04	28.51
W4	−5.97	6.53
A1	−3.83	16.67
A2	−4.83	28.66
A3	−10.85	28.58
A4	−9.83	16.6

Does anything conflict?

- **The new house, the driveway and the paths:** no. The old house is 4.6 m west of the new house's west wall and 3.8 m west of the M line; the driveway (x −3.95 … 0) runs between them and keeps its 3.95 m; the guest path on the driveway's east edge and the fire vehicle's stand are unaffected. The annex's east edge sits on the driveway's west edge (0 m): within the sketch's tolerance; the field check gives the dakka 1.5 m clear.
- **The service yard, the garden, the outdoor kitchen:** all on the east and south; nothing of the old house reaches them.
- **The site plan's "farm beyond the plot" (V8.2):** it placed the old house SOUTH of the build land (y 42–49) with the covered parking, the farm parking and the tank beside it. The deed sketch puts the old house WEST of the driveway (y 5.6–28.5). Either the sketch's building is the "old house" of the brief, or there is a second building in the south: **the owner must say which**; until then the south items stay dotted ("to be measured") and the old-house box of the site plan follows the deed sketch.
- **Peg R (v2: least-squares fitted at x −1.19, y 35.05):** the site plan assumed R at y 48.5 and drew the existing tank "just east of peg R". East of the fitted R is the south garden (y 34–36), 5 m from the new house's south-west corner: the tank's real position must be measured before the garden and the soakaways are fixed.
- **Corner C1:** the deed puts the plot's north-west corner at x −16.7, 10 m further west than the site plan's C1 (−6.5); the septic "near C1" is therefore approximate: to be measured.

Whole-farm study checks passed (6): the 20 deed corners close to the deed area 7 737.85 m² (7737.7 m², rigid transform from UTM) · M1 is the origin and M4 lies on the M line 28.80 m south (28.8) · the well digitised from the deed sketch lies within 2 m of the v2 well (0.84 m): the georeferencing check · the annex's south corner lies within 2 m of the fitted dakka corner D (1.01 m): the sketch and the field agree · the new house's walls lie inside the buildable envelope · the old house (deed sketch) is clear of the new house (6.8 m), the M line (3.8 m) and the driveway's east edge; its annex touches the driveway's west edge (0 m).