
East service block · kitchen, laundry, maid wing, air tower · layout study

Taif / Palm House · Design V3.2 (Z4, Revision 02) · block = CSV x 8.95–13.311, y 0–12.5 (NE corner cut) · 44.73 m² · scale 1 m = 1.3 cm · north up

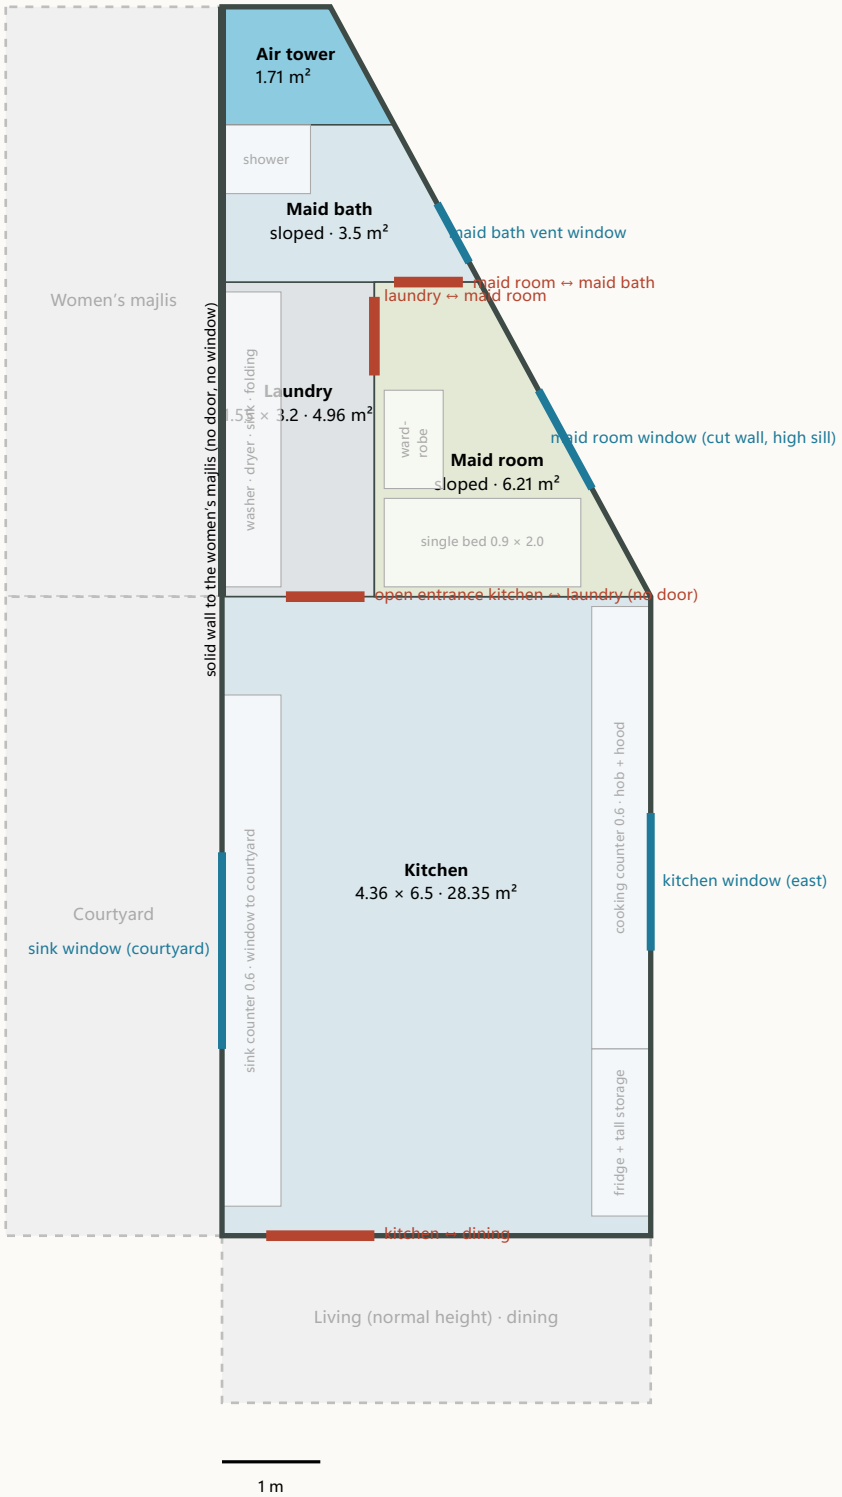

Rooms

Room	w × d (m)	m²
Maid bath	sloped (to the cut wall)	3.5
Maid room	sloped (to the cut wall)	6.21
Laundry	1.55 × 3.2	4.96
Kitchen	4.36 × 6.5	28.35
Air tower (polygon)	4 corners	1.71
Leftover slivers along the cut		0
Block		**44.73**

✓ **All rooms inside the block, no overlaps**

Route

Family: living (normal height) · dining → kitchen (south door).
Maid: kitchen → laundry → maid room → maid bath. No external door and no other door: all her movement passes through the kitchen.
Cooking: sink on the courtyard wall, hob and hood on the east (outside) wall, so heat and smoke leave the house; fridge and tall storage at the south-east, next to the dining door, both on the new east wall face.

Rules

- Kitchen isolated: doors only to the dining area (south) and the laundry (north). No door to the courtyard, riwaq or women's majlis.
- Kitchen 4.361 × 6.5 m on axes (28.35 m², ≈ 4.136 m clear wide), y 6.0–12.5, exactly on the courtyard lines. Sink run on the courtyard wall, hob and hood on the east wall (4.5 m), fridge and tall storage at the south-east; ≈ 2.94 m between the counter lines. No island (only 0.6 m deep would fit); room for a small breakfast table.
- Laundry vertical on the west wall (women's majlis side), 1.55 × 3.2 m (x 0–1.55, y 2.8–6.0), from the kitchen up to the maid bath: open entrance from the kitchen in its south wall (no door); washer, dryer, utility sink and folding counter in one line on the west wall (solid, no opening); ≈ 0.75 m clear beside the 0.6 m machines (check the real appliances); maid room door at the north end of its east wall. The maid's only route. No outside wall: needs a mechanical extract fan to the roof.
- Maid room east of the laundry, from y 2.8 down to y 6.0; the sloped wall runs straight on to its south-east corner (≈ 6.21 m² on centre lines, ≈ 5.10 m² clear, under the 6.5 m² target): door from the laundry at the north end of its west wall and door to the maid bath in its north wall, both in the narrow north part; single bed 0.9 × 2.0 along the south wall (the widest part, 2.81 m) and a wardrobe on the west wall; window in the cut wall with a high sill (lane side, privacy).
- Main cross walls on the house lines: y 6.0 (women's majlis / courtyard) and y 12.5 (dining).
- Maid bath 1.6 m deep, running up to the cut wall (≈ 3.50 m²): WC, basin, compact shower; vent window in the cut wall; door only from the maid room.
- Solid wall (no door, no window) between the maid wing and the women's majlis.
- Air tower in the tip of the cut corner (≈ 1.71 m² on centre lines, ≈ 1.1 m² clear), takes no room space; cleaning from a roof hatch.
- One east wet stack: maid bath, laundry sink and kitchen sink on one drain line down the block; cleanout access in the laundry.

Edit the lists at the top: rooms-data, fixtures, doors, windows, solid, neighbours. Main CSV = local + (8.95, 0).