
West wash block · family + guest · layout study

Taif / Palm House · Design V3.2 (Z4, Revision 02) · block 2.75 × 13.1 m = 36.03 m² · scale 1 m = 1.7 cm · north up

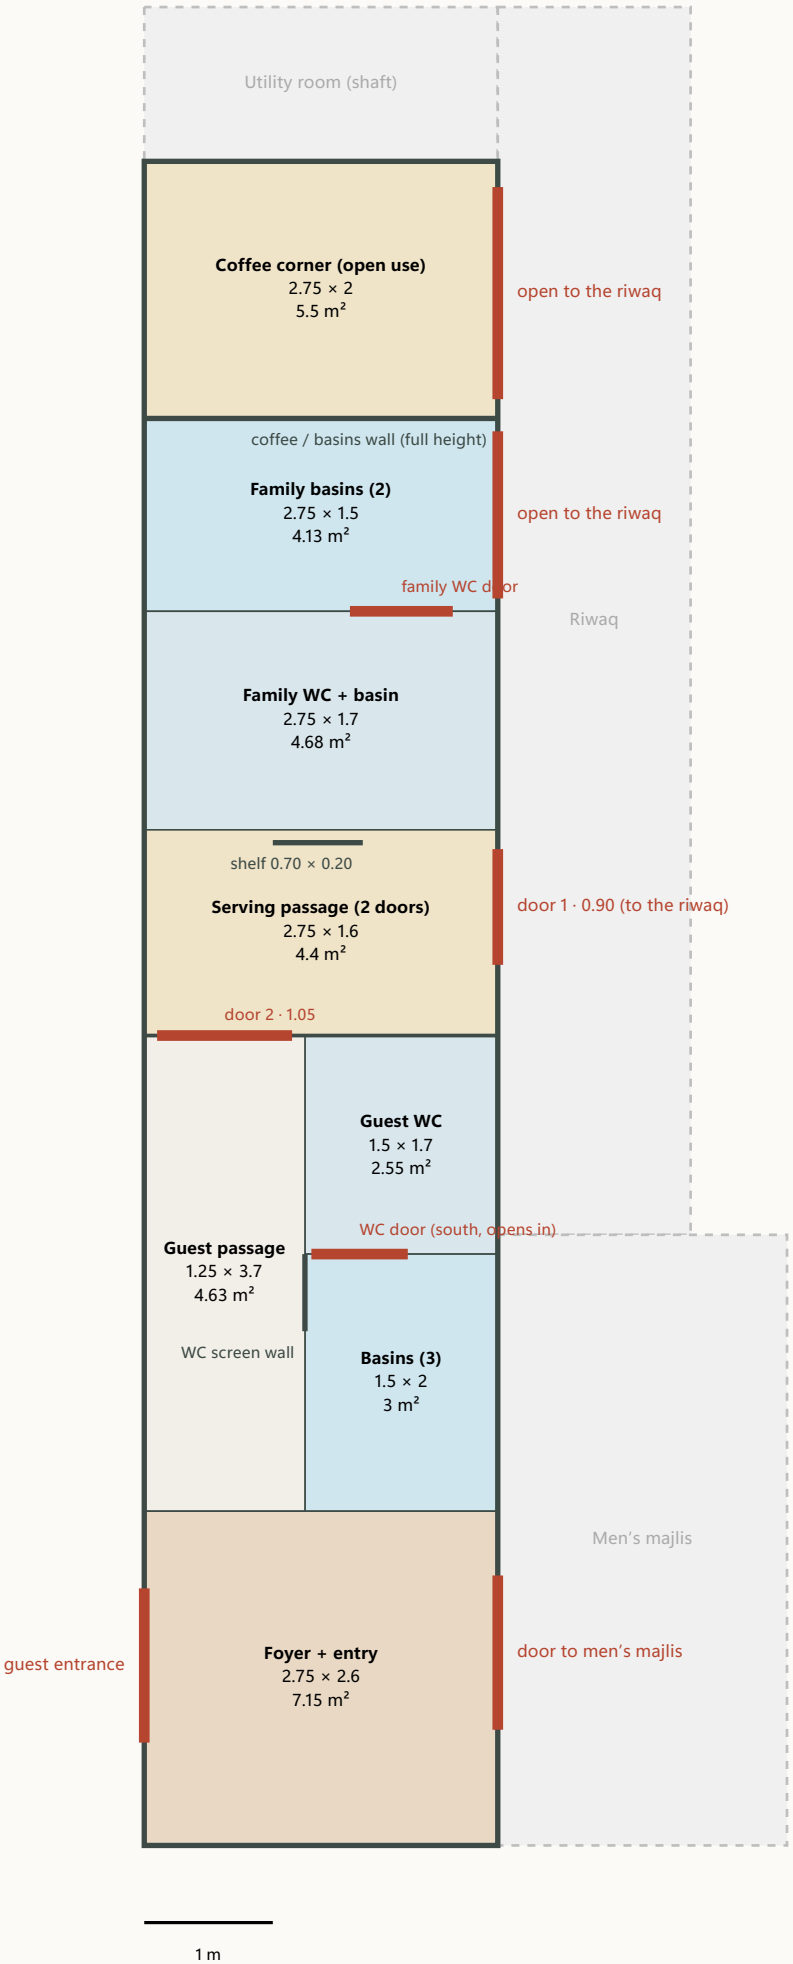

Rooms

Room	w × d (m)	m²
Coffee corner (open use)	2.75 × 2	5.5
Family basins (2)	2.75 × 1.5	4.13
Family WC + basin	2.75 × 1.7	4.68
Serving passage (2 doors)	2.75 × 1.6	4.4
Guest WC	1.5 × 1.7	2.55
Basins (3)	1.5 × 2	3
Guest passage	1.25 × 3.7	4.63
Foyer + entry	2.75 × 2.6	7.15
Block	2.75 × 13.1	**36.03**

✓ **All rooms inside the block, no overlaps, no gaps**

Route

Guests: entrance → foyer → majlis; for washing, foyer → guest passage (west) → basins and WC (east).
Family: riwaq → family basins (open, no door) → family WC (door off the basins) · coffee corner (open to the riwaq only; a full-height wall separates it from the basins).
Serving: coffee corner or kitchen → riwaq → **serving passage** (door 1, shelf, door 2) → guest passage → foyer → majlis.
The serving passage is the ONLY link between the family and guest sides, with only two doors: the family opens door 1 from the riwaq, puts coffee, trays or food on the shelf, closes door 1 and calls the host; the host opens door 2 from the guest passage, collects and closes it. The two doors are never open together. Bent entry (majaz): an open door 2 shows only the passage, the blank south wall of the family WC and the closed door 1 at the far end. The guest side has no door onto the riwaq.
Doors in the whole block: family WC, serving doors 1 and 2, guest WC, guest entrance, majlis door. No corridor doors.

Rules

- One strip of wet rooms on one drain run: coffee-corner sink, family basins, family WC, guest WC, guest basins. Family WC and guest WC sit 1.1 m apart; the drain crosses under the serving passage floor (1.6 m deep), with a cleanout access point there. First-floor bathrooms should stack over the north part of the block, near the shaft.
- Family / guest line at y = 6.8: crossed only through the serving passage (2.75 × 1.6 on axes, 1.40 m between walls): a shelf 0.70 × 0.20 on its north wall and 1.20 m clear in front of it. Door 1 0.90 m, door 2 1.05 m. Door 1 locks from the riwaq side and door 2 from inside the passage, so the family controls both.
- Door 1 is at the passage's east end, on the riwaq. Opposite it the living room now has a 1.20 m low partition (open above), so it is no full screen for someone standing: family privacy relies on the two doors never being open together.
- Family WC full width (2.75 × 1.7 = 4.68 m²): WC and basin; a small shower (≈ 0.9 × 0.9) still fits at one end. Its door is off the basin niche, so the open family door never faces it.
- Family basins (2): an open niche on the riwaq (2.75 × 1.5), no door; a full-height wall separates it from the coffee corner.
- Coffee corner (2.75 × 2.0, open use, still to decide): one counter along the north wall with a small sink, kettle and coffee things, and an under-counter fridge. Open to the riwaq on its east side only.
- The guest WC holds a WC only (and a hand spray). Its door is in the south wall at the west end, opening inwards, clear of the basin counter on the east wall (≈ 0.55 m deep).
- The guest WC west wall continues 0.6 m south as a screen: from the passage the WC door is out of sight, but the basins stay open.
- Three guest basins in one row (≈ 0.6 m each) along the east wall, open to the passage (≈ 1.025 m clear).
- V3.2: the guest WC, basins, guest passage and foyer moved 0.50 m south as one block (sizes unchanged); the south facade is 0.50 m further south.