
West wash block · family + guest · layout study

Taif / Palm House · Ground floor V10.0 (the owner's review, 10 Nov 2026) · block 2.75 × 13.6 m = 37.4 m² · scale 1 m = 1.35 cm · north up

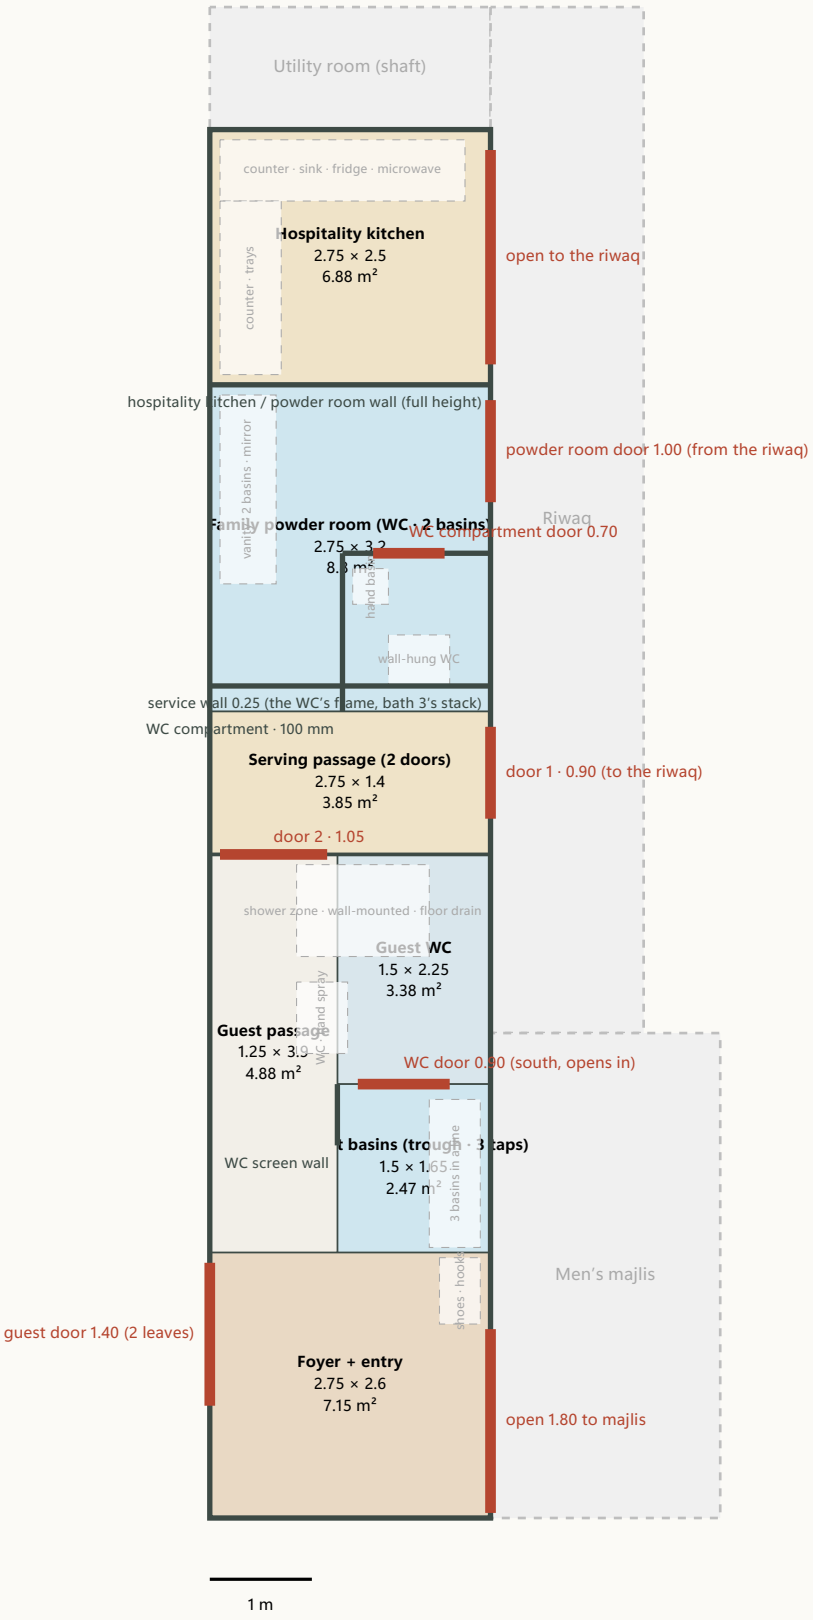

Rooms

Room	w × d (m)	m²
Hospitality kitchen	2.75 × 2.5	6.88
Family powder room (WC · 2 basins)	2.75 × 3.2	8.8
Serving passage (2 doors)	2.75 × 1.4	3.85
Guest WC	1.5 × 2.25	3.38
Guest basins (trough · 3 taps)	1.5 × 1.65	2.47
Guest passage	1.25 × 3.9	4.88
Foyer + entry	2.75 × 2.6	7.15
Block	2.75 × 13.6	**37.4**

✓ **All rooms inside the block, no overlaps, no gaps**

Route

Guests: double door (north end of the foyer's west wall) → foyer: shoes and bisht on the wall opposite → turn south → 1.80 m opening into the men's majlis (south end of the east wall). For washing: foyer → guest passage → trough basin and WC.
Family: riwaq → hospitality kitchen (open, no door) · the family **powder room** (one door from the riwaq; the two basins under the mirror in the open zone facing the door, the WC in its own compartment at the far end with its own door and a hand basin).
Serving: hospitality kitchen or main kitchen → riwaq → door 1 → **serving passage** → door 2 → guest passage → foyer → majlis. The two doors are never open together: the family leaves the tray, closes door 1 and calls the host; the host opens door 2 and collects. Door 1 locks from the riwaq side, door 2 from inside the passage, so the family controls both. The guest side has no door onto the riwaq.

Rules

- Hospitality kitchen 2.75 × 2.5 (≈ 5.8 m² clear): light (clean) kitchen for coffee, tea, dates, desserts and reheating; the serving base for the men's majlis. Open to the riwaq, no door, no hob. L-counter on the north and west walls with a small sink, under-counter fridge, microwave, kettle and coffee things; cups and trays stored there; small extract fan. The main east kitchen is the heavy (dirty) kitchen.
- A full-height wall separates the hospitality kitchen from the powder room; the kitchen opens only to the riwaq, the powder room has its own door.
- **Family powder room 2.75 × 3.2 (≈ 7.6 m² clear; 10 Nov 2026, owner: simple and straight):** the **WC compartment** (x 1.3–2.75, y 14.55–16.1 CSV, ≈ 1.3 × 1.4 clear; 100 mm partitions; its own 0.70 door opening north into the room) holds **only the WC and one basin** (the wall-hung WC on the south 0.25 service wall with its frame and bedroom 3's stack, an access panel from the serving passage; the basin on the compartment's west partition); **outside, in the open zone in front of the entrance** (the door 1.00 from the riwaq, x 2.75, y 13.05–14.05 CSV), a vanity with **two basins under a large mirror** on the west wall (1.85 m), cove lighting; **no shower** on the ground floor (owner). The drains 0.5 m into the west buried run; the hidden beam B14 (y 14.4) becomes a drop beam or the slab spans 3.2 m (the engineer).
- Serving passage 2.75 × 1.4 on axes, 1.20 m clear, no shelf and no fixed equipment; door 1 0.90 m to the riwaq, door 2 1.05 m to the guest passage. Opposite door 1 the living's west wall is solid and full height (the TV wall, V6.3); privacy rests on the two doors.20 m low partition, so privacy rests on the two doors.
- **Guest WC 1.5 × 2.25 (≈ 1.3 × 2.05 clear; 10 Nov 2026, owner: simple):** inside **only the WC and a wall-mounted shower with mixer** on the north wall over a floor drain with falls, **a wet room** tanked and tiled to the ceiling, **no basin, no cubicle wall, no tray**; the WC with its hand spray at the south-west, clear of the door's swing (the shower zone 1.3 × 0.9 at the north end); the door 0.90 in the south wall (y 19.75 CSV), opening in, hidden from the passage by the 0.6 m screen wall.
- Guest basins 1.5 × 1.65 (≈ 1.3 × 1.45 clear; 10 Nov 2026): directly in front of the WC, **three basins in one straight line** on the east wall (1.45 m: three bowls at 0.45 m, or one trough with three taps), a mirror above, open to the guest passage (≈ 1.025 m clear); the guests wash here and the WC's door stays hidden behind the screen wall.
- Foyer 2.75 × 2.6: double door 1.40 m (two leaves, opening in) at the north end of the west wall; 1.80 m opening, no door, at the south end of the east wall (≈ 0.65 m of wall left at its north end for the shoe cabinet and hooks). The two openings overlap by ≈ 0.75 m along the foyer, so the bent entry is only partial: from the

door a guest sees a strip of the majlis; a curtain or a short screen in front of the opening would close it.

- One strip of wet rooms on one drain run, the west buried run (hospitality kitchen sink, the powder room's three basins and WC, the guest WC's floor drain and WC, the three guest basins), cleanout under the serving passage. First-floor bathrooms stack over the north part of the block, near the shaft.